
GLOBAL CASORETTO · INTERVENTO 6 · CONCEPT


Viale Lombardia

Da piazza Durante a piazzale Piola, circa 850 m di viale alberato largo 30 m tra le facciate, oggi occupato dalle auto anche sui marciapiedi. Il progetto porta il limite a 30 km/h, stringe le corsie e fa correre su entrambi i lati una ciclabile protetta, tra i bagolari e le auto in sosta a strisce blu. I marciapiedi tornano a chi cammina e tutti gli alberi restano.

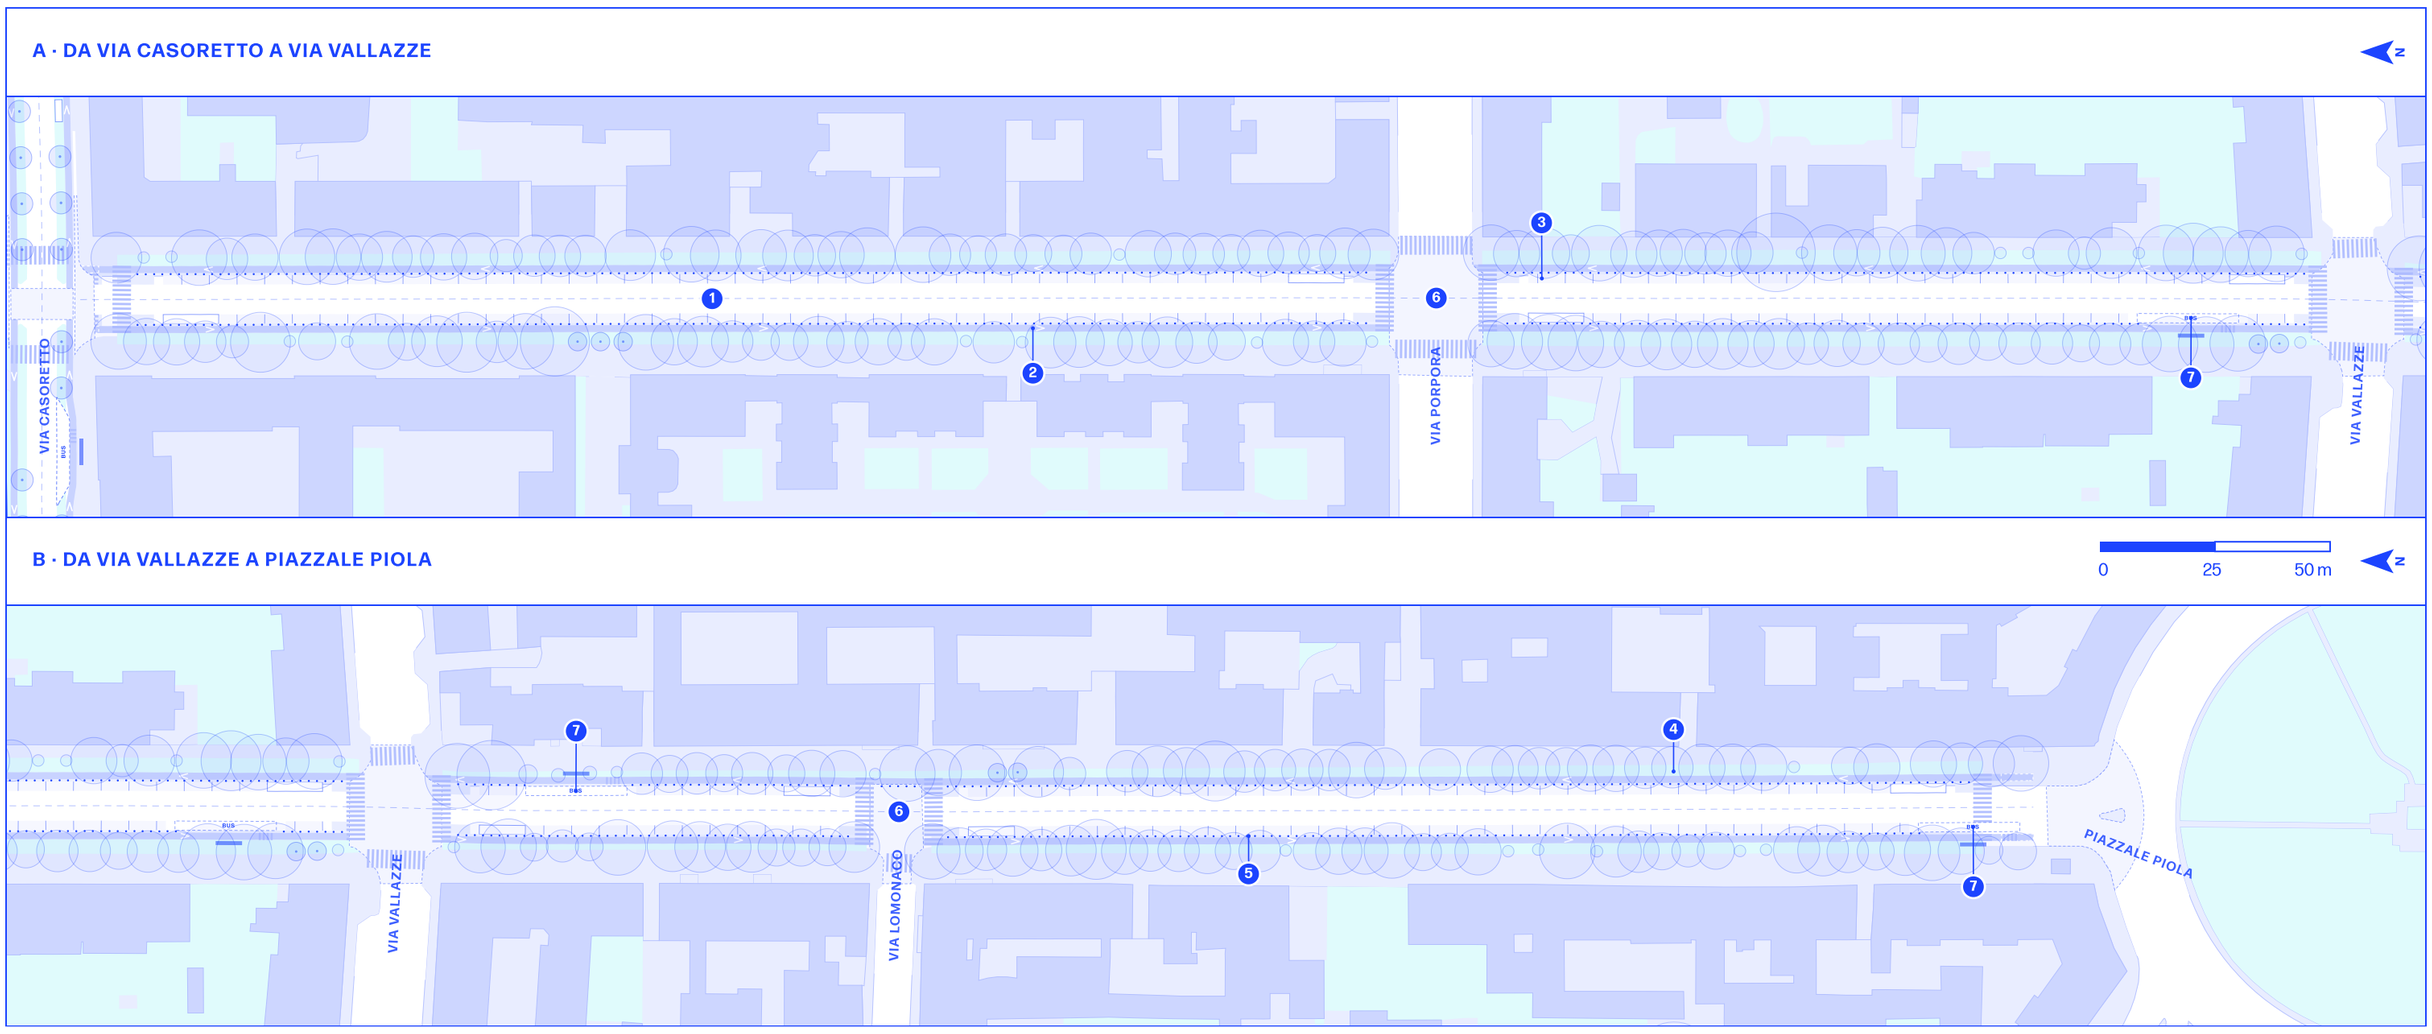

Sezione tipo

Viale Lombardia tra via Casoretto e via Porpora, circa 30 m tra le facciate · misure in metri dalla carta tecnica del Comune

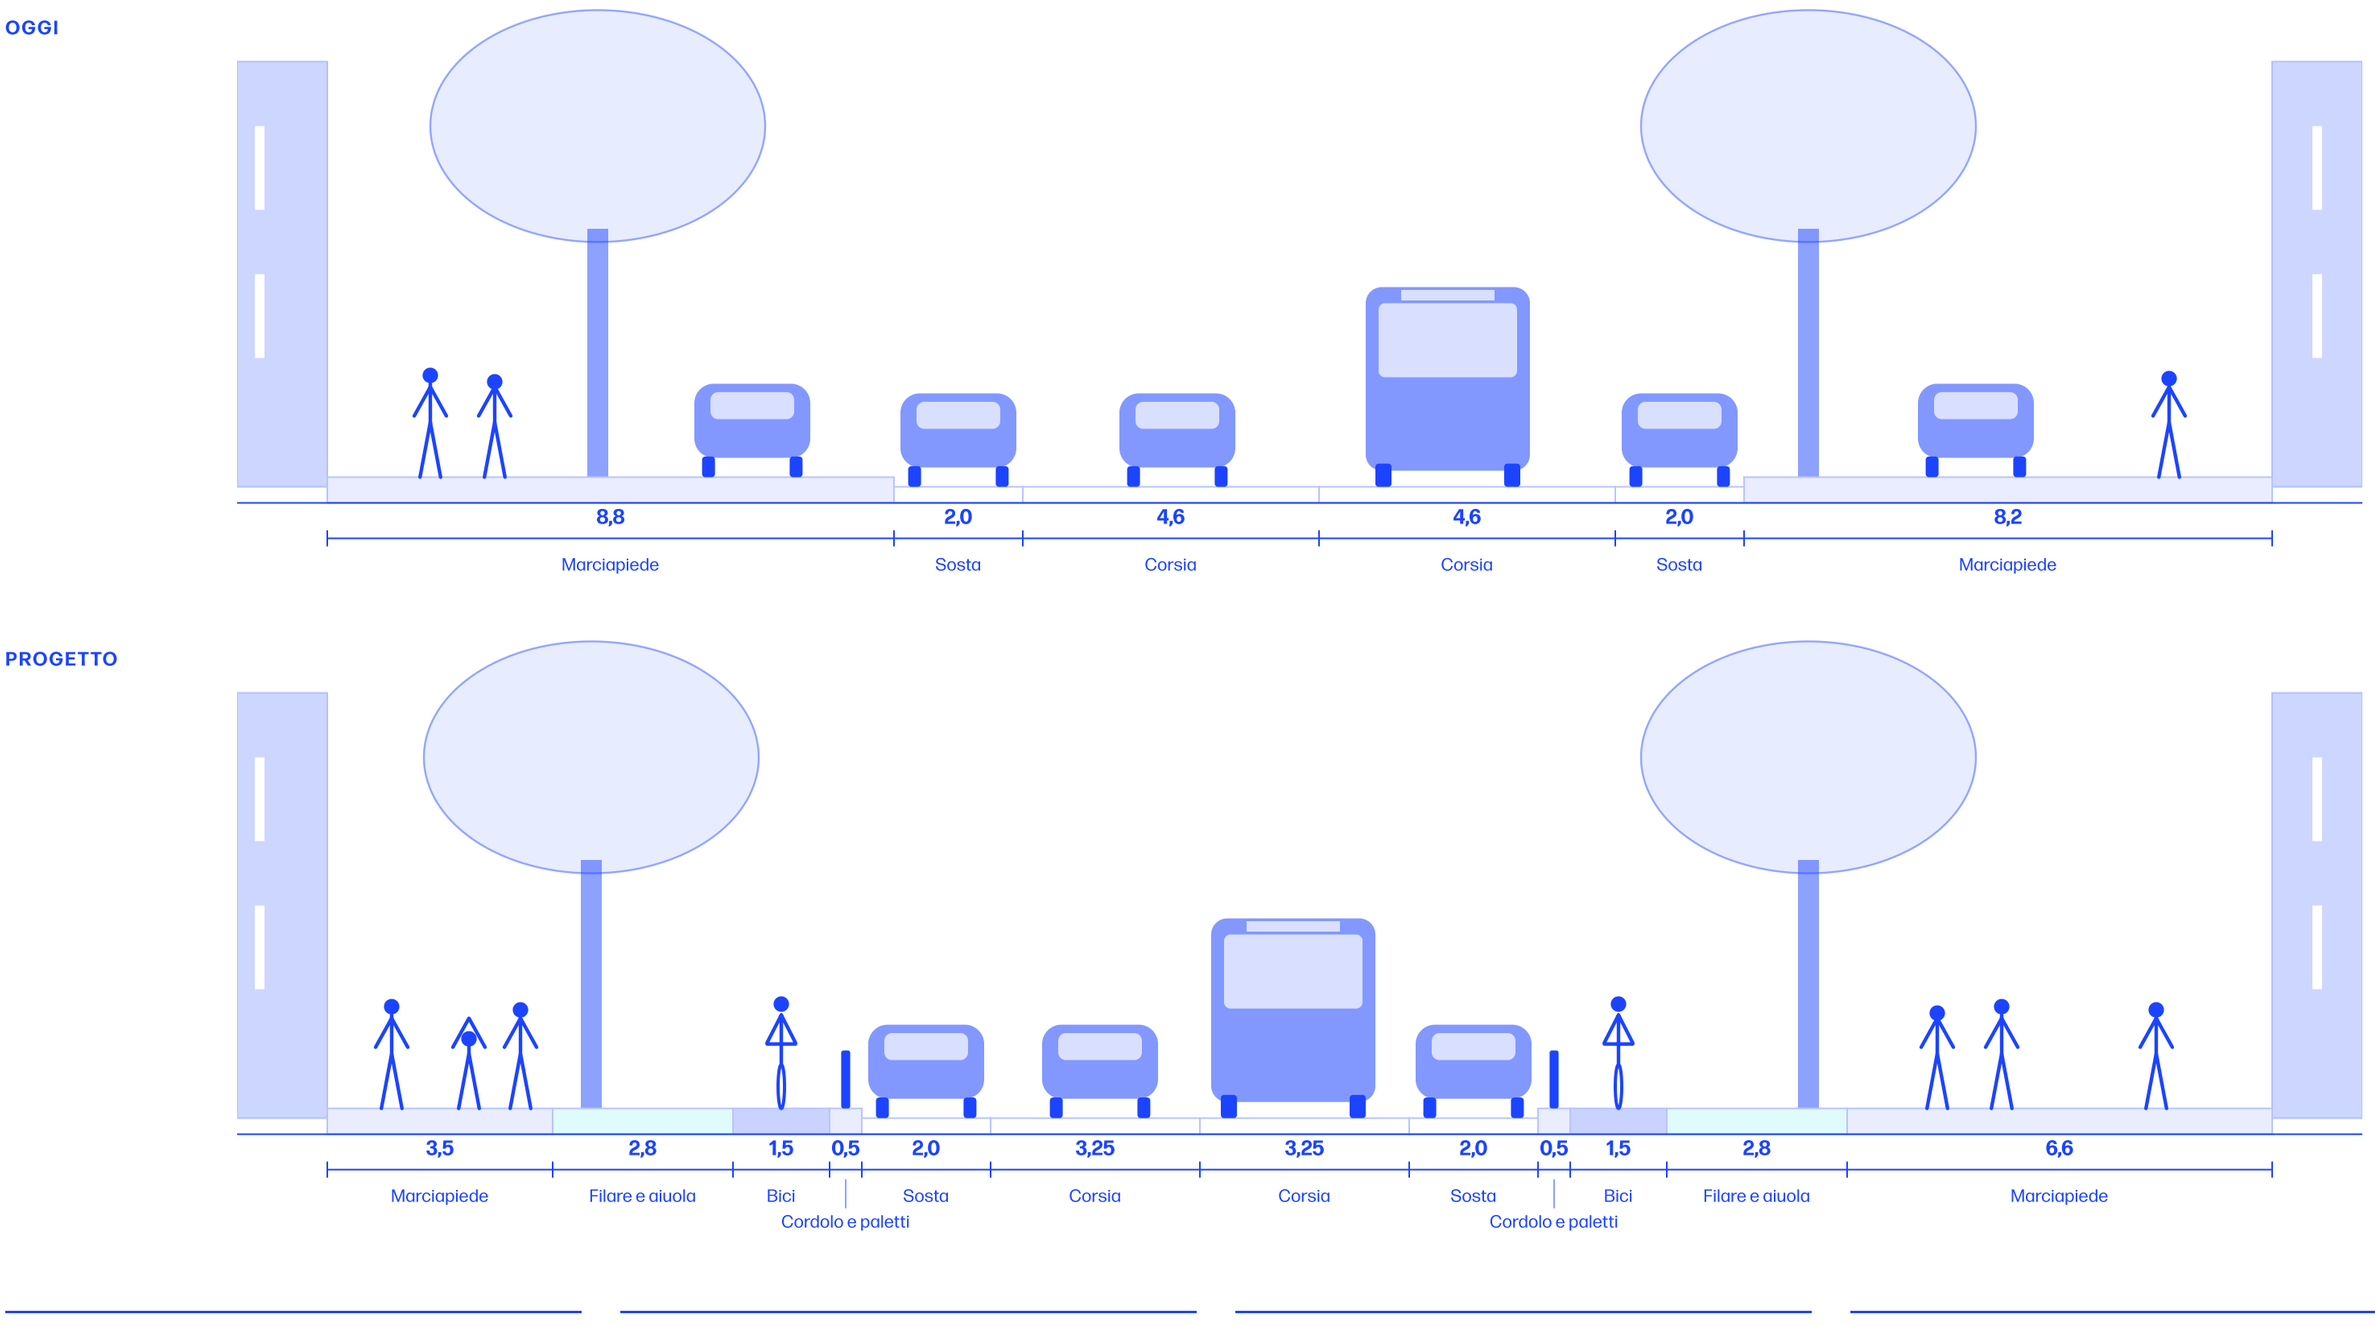

1 Strada a 30 km/h

Doppio senso su due corsie da 3,25 m, quanto serve agli autobus 39 e 62, che percorrono il viale da via Porpora a piazzale Piola. Oggi le corsie sono larghe più di 4,5 m e invitano a correre.

2 Ciclabile protetta

Una corsia bici da 1,5 m per senso di marcia, alla quota del marciapiede, tra il filare e le auto in sosta. Un cordolo da 0,5 m la tiene lontana dalle portiere.

3 Sosta a strisce blu

Le auto restano lungo la strada, in linea e regolate, e fanno da barriera tra traffico e bici: circa 210 posti su tutto il viale. In ogni isolato due stalli per lato, vicino agli incroci, sono riservati al carico e scarico merci (8 piazzole).

4 Filari e aiuole

Restano tutti i 248 bagolari. Il filare diventa un'aiuola continua, larga fino a 3 m, che raccoglie l'acqua piovana; 7 nuovi alberi chiudono i vuoti.

5 Paletti dissuasori

Una fila continua di paletti sul cordolo, interrotta solo agli attraversamenti e alle fermate, impedisce alle auto di salire su ciclabile e marciapiede. Dietro il filare il marciapiede torna tutto a chi cammina.

6 Incroci rialzati

A ogni incrocio la strada sale alla quota del marciapiede, con le strisce su tutti i lati. Dove finisce la sosta il marciapiede si allarga e l'attraversamento si accorcia.

7 Fermate del bus

Tre fermate di 39 e 62: prima di via Vallazze nei due sensi e prima di piazzale Piola. Sono in rientro nella fascia di sosta: il bus si ferma senza bloccare il traffico e la ciclabile passa davanti alla pensilina, con le strisce.

Strada a 30 km/h · Ciclabile · Sosta a strisce blu · Carico e scarico · Filare e aiuola · Paletti dissuasori · Incrocio rialzato · Strisce pedonali · Fermata bus · Albero nuovo · Albero esistente

Schema di concept · Base cartografica: Comune di Milano, Database Topografico 2020 · Alberi esistenti: Comune di Milano, open data (marzo 2025) · Fermate e linee: ATM, open data del Comune di Milano