
GLOBAL CASORETTO · INTERVENTO 7 · CONCEPT


Via Teodosio

Da piazza Sire Raul a via Pacini, circa 1 km di via alberata larga 30 m tra le facciate, oggi occupata dalle auto anche sui marciapiedi. Il progetto porta il limite a 30 km/h, stringe le corsie e fa correre su entrambi i lati una ciclabile protetta, tra i bagolari e le auto in sosta a strisce blu. I marciapiedi tornano a chi cammina e tutti gli alberi restano.


A · DA PIAZZA SIRE RAUL A VIA CASORETTO

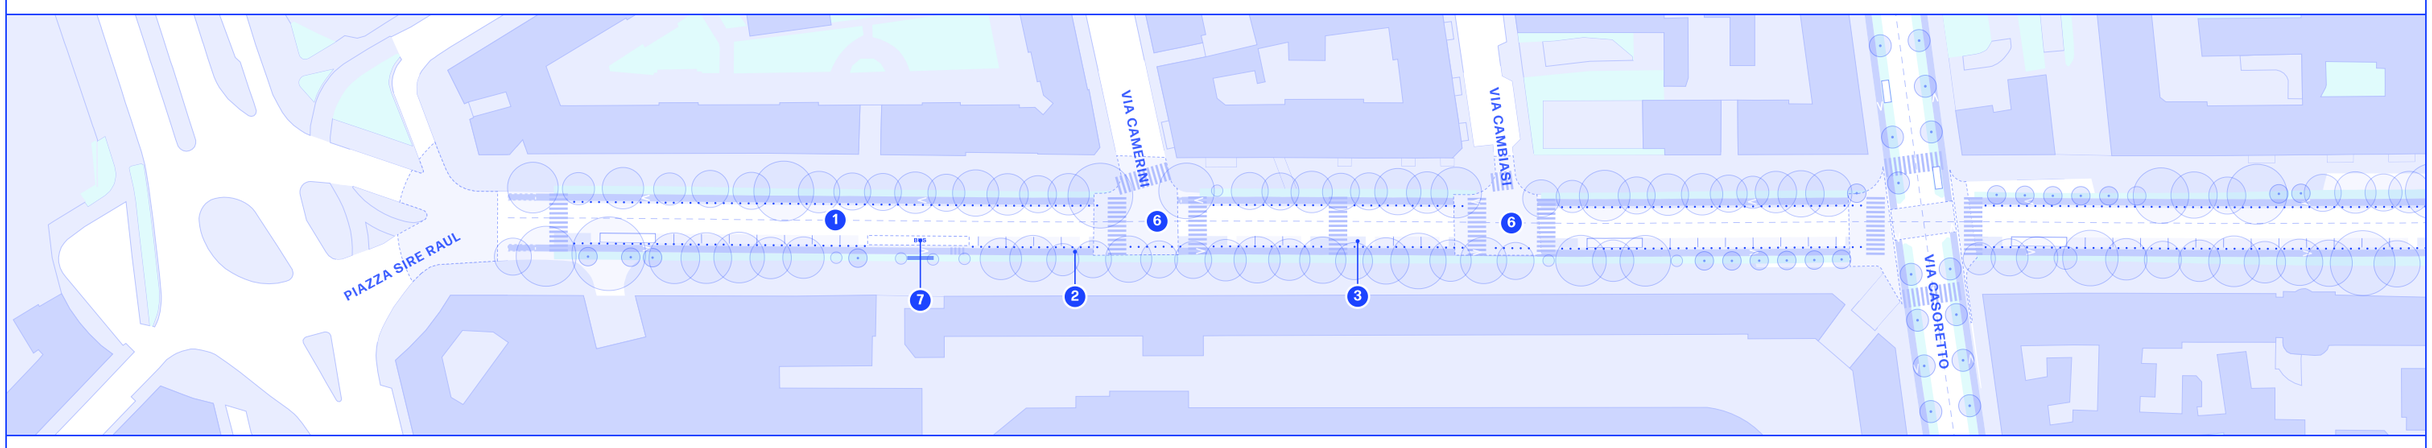

B · DA VIA CASORETTO A VIA PORPORA

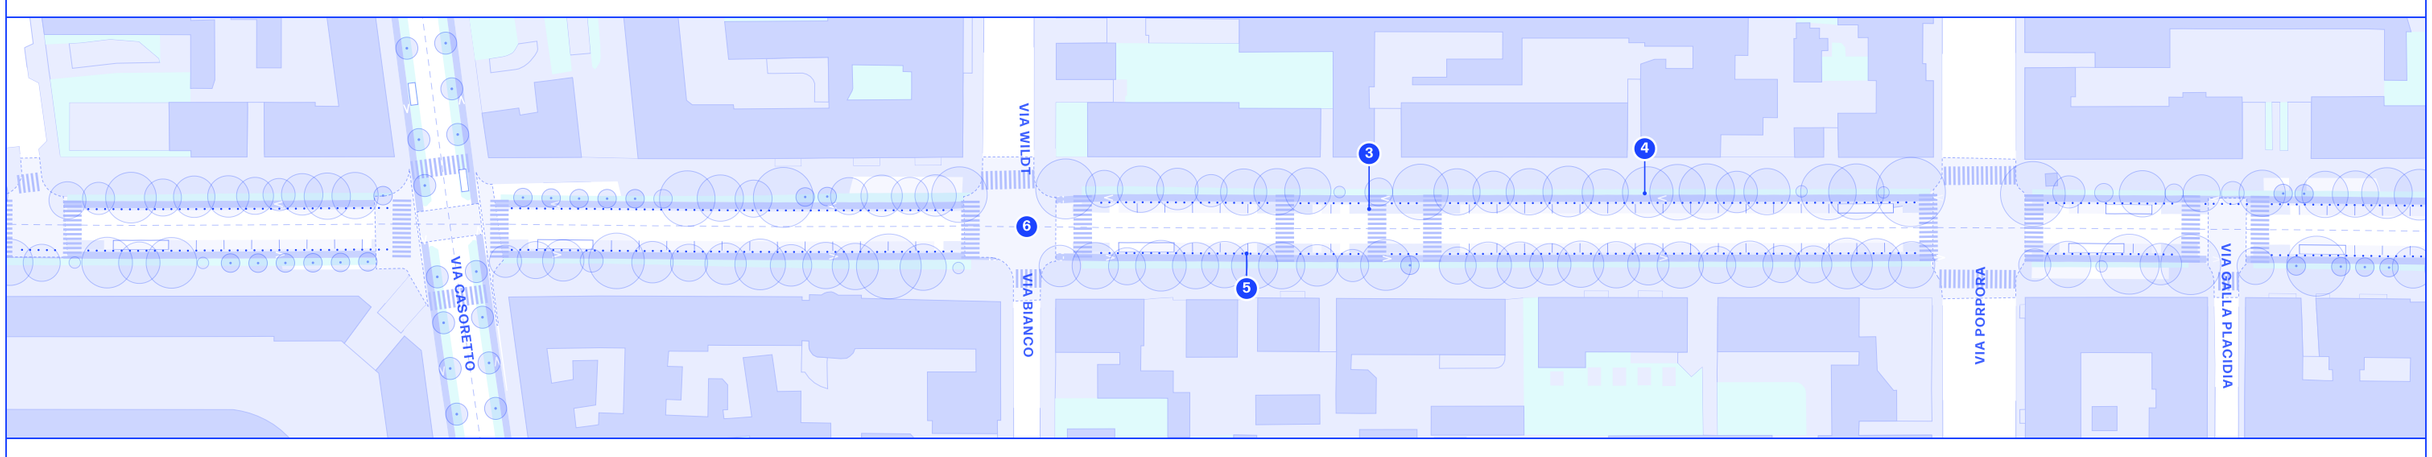

C · DA VIA PORPORA A VIA PACINI

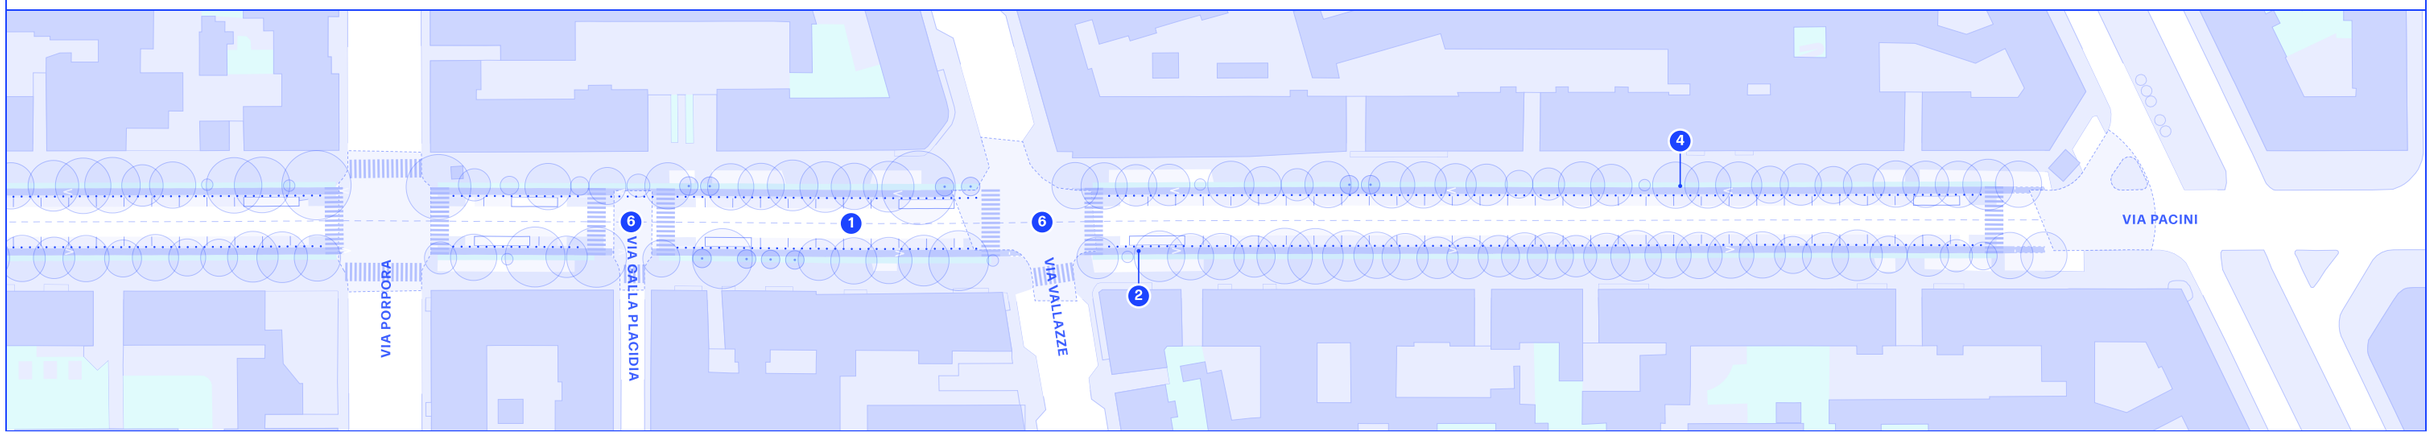


0 25 50 m


Sezione tipo

Via Teodosio tra via Wildt e via Porpora, circa 31 m tra le facciate · misure in metri dalla carta tecnica del Comune

OGGI

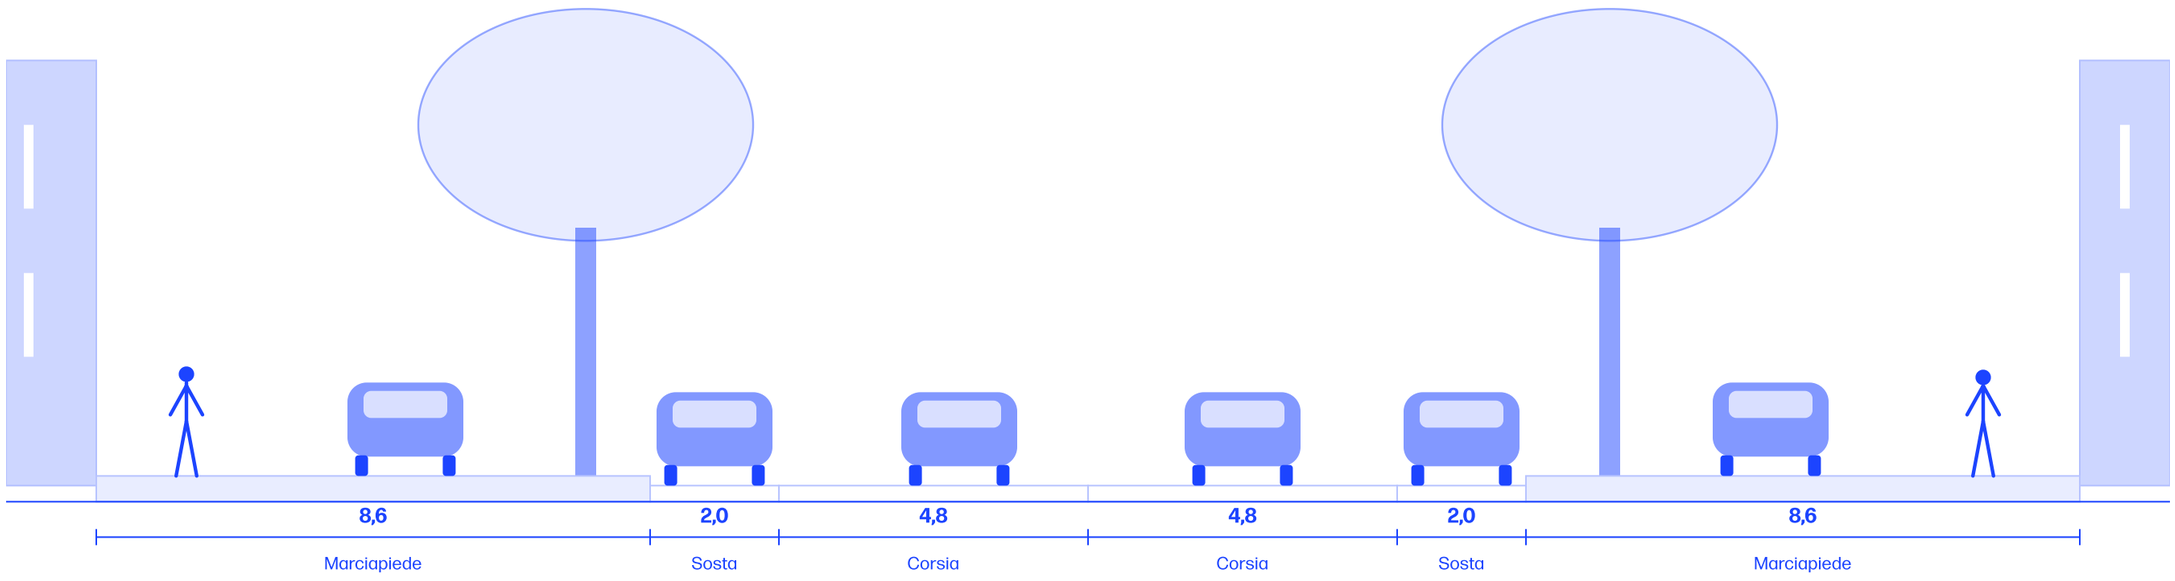

PROGETTO

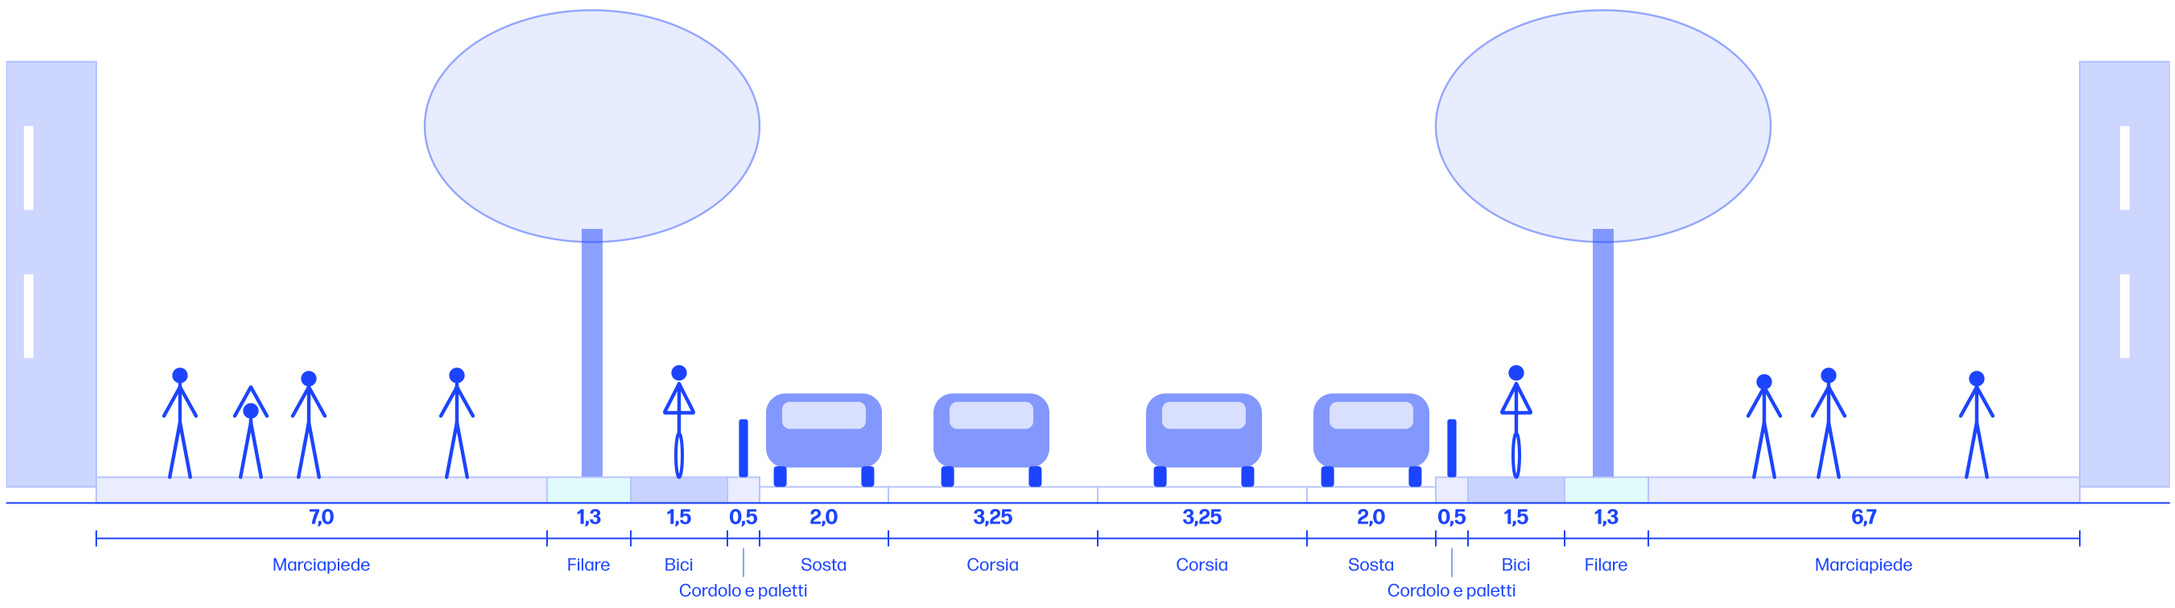

1 Strada a 30 km/h

Doppio senso su due corsie da 3,25 m, quanto serve all'autobus 62, che percorre la via da piazza Sire Raul a via Casoretto. Oggi le corsie sono larghe quasi 5 m e invitano a correre.

2 Ciclabile protetta

Una corsia bici da 1,5 m per senso di marcia, alla quota del marciapiede, tra il filare e le auto in sosta. Un cordolo da 0,5 m la tiene lontana dalle portiere.

3 Sosta a strisce blu

Le auto restano lungo la strada, in linea e regolate, e fanno da barriera tra traffico e bici: circa 140 posti, più 11 piazzole di carico e scarico vicino agli incroci. Da piazza Sire Raul all'incrocio con via Wildt e via Bianco i filari sono più vicini e la sosta resta su un solo lato.

4 Filari e aiuole

Restano tutti i 240 bagolari. Il filare diventa un'aiuola continua che raccoglie l'acqua piovana; 29 nuovi alberi chiudono i vuoti.

5 Paletti dissuasori

Una fila continua di paletti sul cordolo, interrotta solo agli attraversamenti e alle fermate, impedisce alle auto di salire su ciclabile e marciapiede. Dietro il filare il marciapiede, largo circa 7 m, torna tutto a chi cammina.

6 Incroci rialzati

A ogni incrocio la strada sale alla quota del marciapiede, con le strisce su tutti i lati. Dove finisce la sosta il marciapiede si allarga e l'attraversamento si accorcia.

7 Fermata del bus

La fermata del 62 dopo piazza Sire Raul è in rientro nella fascia di sosta: il bus si ferma senza bloccare il traffico e la ciclabile passa davanti alla pensilina, con le strisce.

Strada a 30 km/h · Ciclabile · Sosta a strisce blu · Carico e scarico · Filare e aiuola · Paletti dissuasori · Incrocio rialzato · Strisce pedonali · Fermata bus · Albero nuovo · Albero esistente

Schema di concept · Base cartografica: Comune di Milano, Database Topografico 2020 · Alberi esistenti: Comune di Milano, open data (marzo 2025) · Fermate e linee: ATM, open data del Comune di Milano